


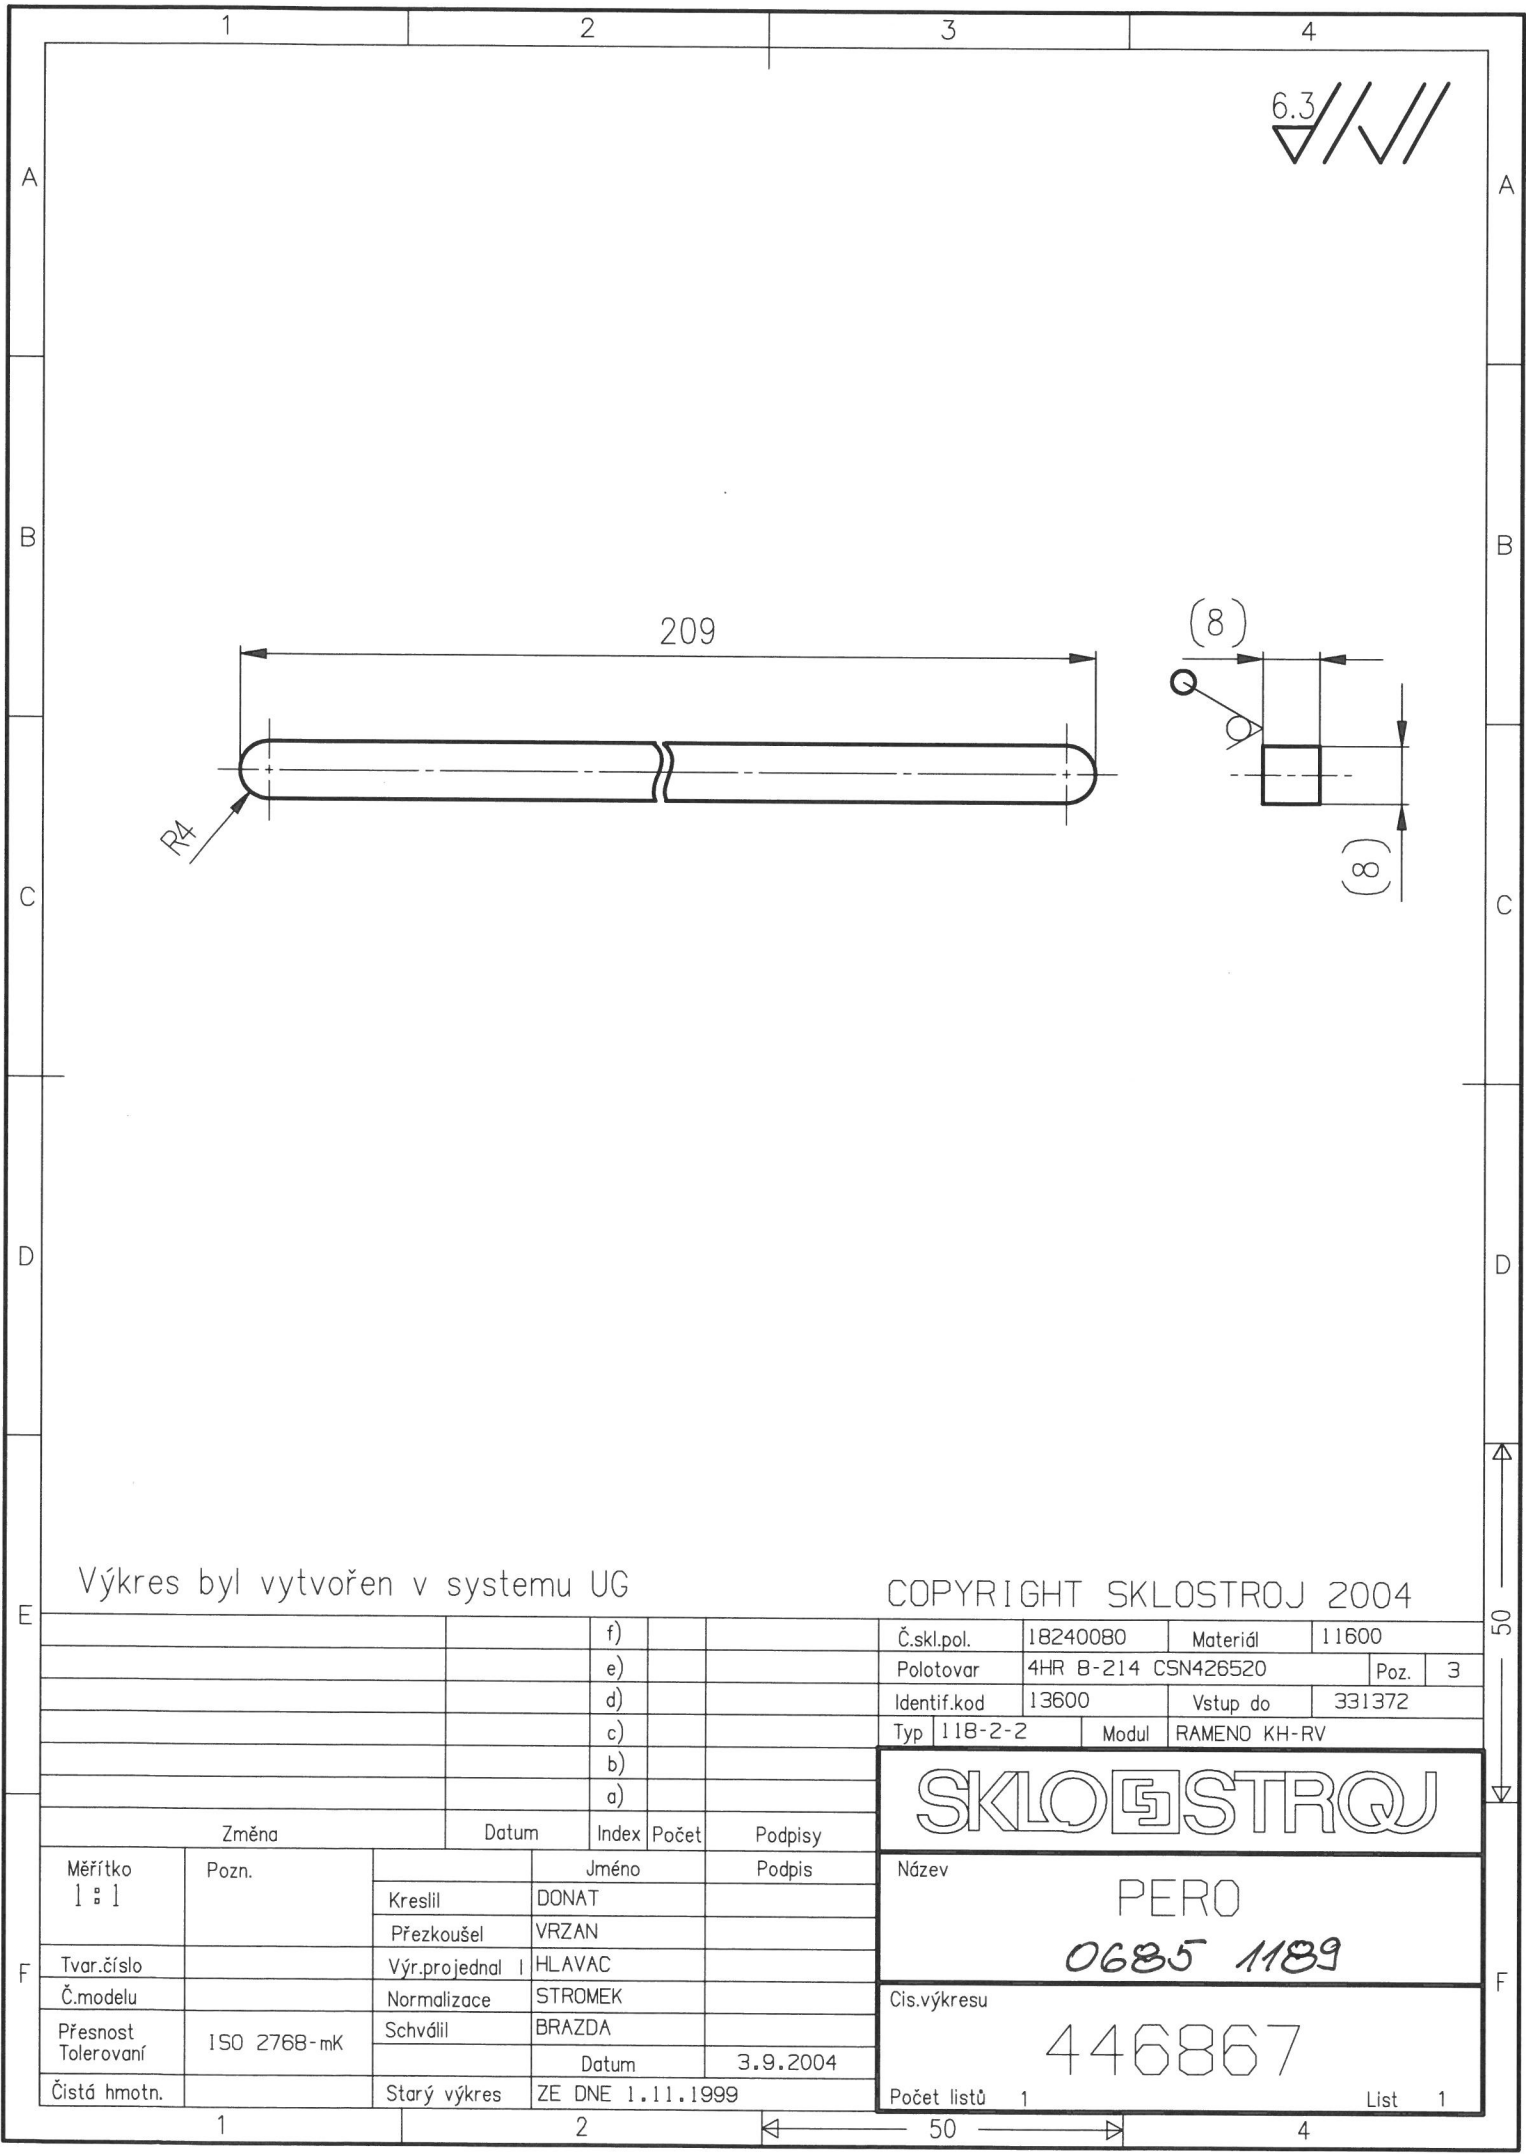

6.3

209

R4

(8)

(8)

Výkres byl vytvořen v systému UG

COPYRIGHT SKLOSTROJ 2004

|                     |             |               |  |                  |       |          |                      |                                                                  |                     |  |          |  |              |  |
|---------------------|-------------|---------------|--|------------------|-------|----------|----------------------|------------------------------------------------------------------|---------------------|--|----------|--|--------------|--|
|                     |             |               |  | f)               |       |          | Č.skl.pol.           |                                                                  | 18240080            |  | Materiál |  | 11600        |  |
|                     |             |               |  | e)               |       |          | Polotovár            |                                                                  | 4HR 8-214 CSN426520 |  | Poz.     |  | 3            |  |
|                     |             |               |  | d)               |       |          | Identif.kod          |                                                                  | 13600               |  | Vstup do |  | 331372       |  |
|                     |             |               |  | c)               |       |          | Typ                  |                                                                  | 118-2-2             |  | Modul    |  | RAMENO KH-RV |  |
|                     |             |               |  | b)               |       |          | <div>SKLOSTROJ</div> |                                                                  |                     |  |          |  |              |  |
|                     |             |               |  | a)               |       |          |                      |                                                                  |                     |  |          |  |              |  |
| Změna               |             | Datum         |  | Index            | Počet | Podpisy  |                      | <div>Název</div> <div>PERO</div> <div>0685 1189</div>            |                     |  |          |  |              |  |
| Měřítka             | Pozn.       |               |  | Jméno            |       | Podpis   |                      |                                                                  |                     |  |          |  |              |  |
| 1 : 1               |             | Kreslil       |  | DONAT            |       |          |                      | <div>Cis.výkresu</div> <div>446867</div>                         |                     |  |          |  |              |  |
|                     |             | Přezkoušel    |  | VRZAN            |       |          |                      |                                                                  |                     |  |          |  |              |  |
| Tvar.číslo          |             | Výr.projednal |  | HLAVAC           |       |          |                      | <div>Počet listů</div> <div>1</div> <div>List</div> <div>1</div> |                     |  |          |  |              |  |
| Č.modelu            |             | Normalizace   |  | STROMEK          |       |          |                      |                                                                  |                     |  |          |  |              |  |
| Přesnost Tolerování | ISO 2768-mK | Schválil      |  | BRAZDA           |       |          |                      |                                                                  |                     |  |          |  |              |  |
|                     |             |               |  | Datum            |       | 3.9.2004 |                      |                                                                  |                     |  |          |  |              |  |
| Čistá hmotn.        |             | Starý výkres  |  | ZE DNE 1.11.1999 |       |          |                      |                                                                  |                     |  |          |  |              |  |