
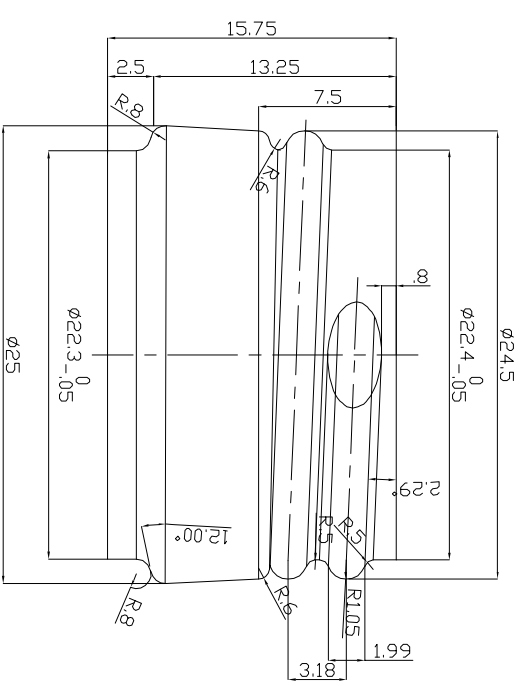
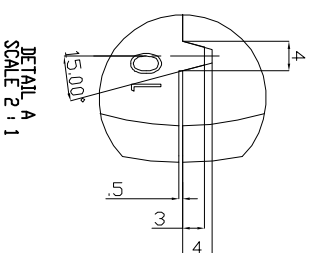
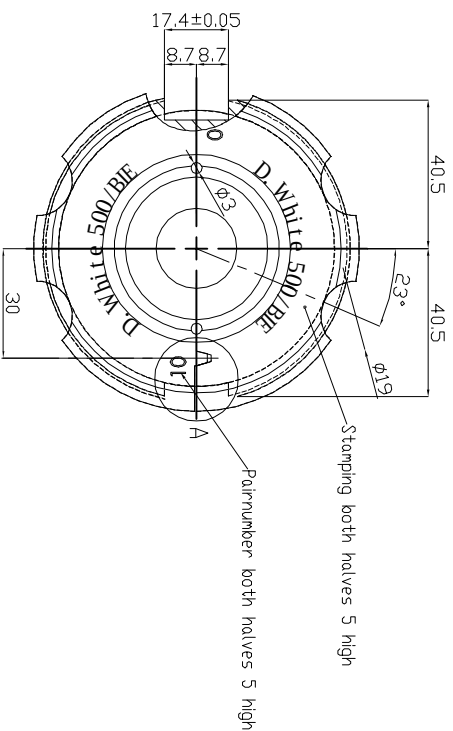
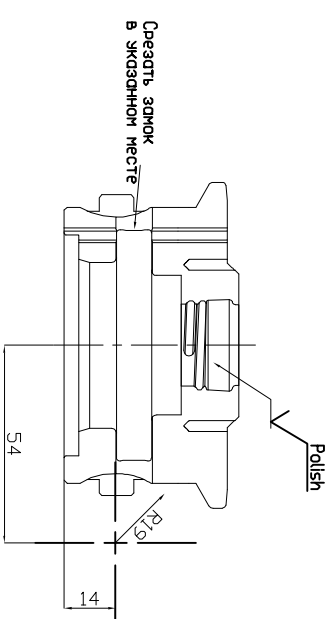
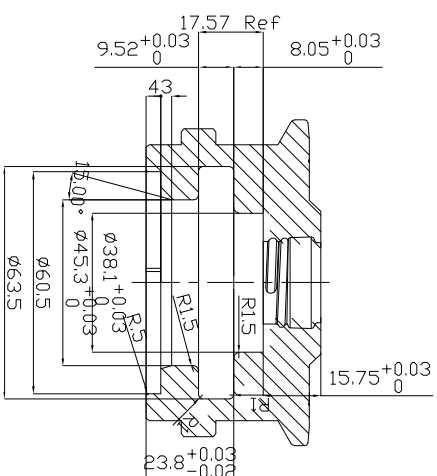


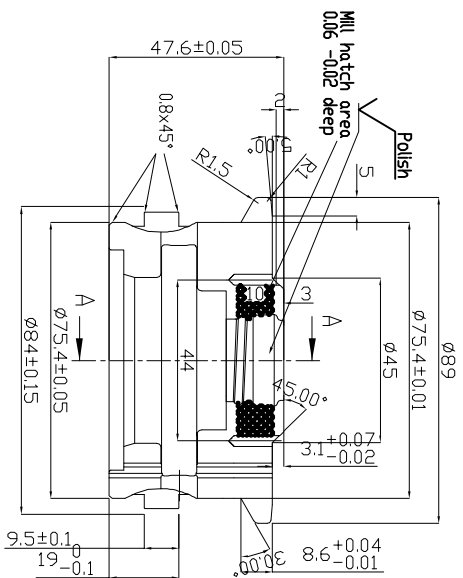

Hard weld cavity 1.5 mm deeper than biggest diameter

INVERT CENTRE : -
'H' DIMENSION : -
ASSEMBLY : -
SCALE : 1:1

DO NOT SCALE DRAWING IF IN DOUBT, ASK				Rev 1 22.10.2015 dra. 22.5 hr	
TOLERANCES UNLESS SPECIFIED DIMENSIONS FOR CAST IRON REMOVE BIRMS & SHARP EDGES IN ACCORDANCE TO STANDARD PRACTICE		JOB NAME	D White 500		
 THIRD ANGLE PROJECTION		ITEM	NECKRING		
		CUSTOMER			
		ORDER NO.	-		
		MATERIAL	CI		
		MACHINE	BPF BB DG 5 1/2"		
CAST ~~~~~ ROUND ~~~~~ V FINE FV POLISH ~~~~~ SURFACE FINISH		QUANTITY			
		REF. NO.			
		DRAWN BY	DN		
		CHECKED BY			
		DATE	26/05/09		
			REVISING		
			DRG No: BIE1032-08-1		