
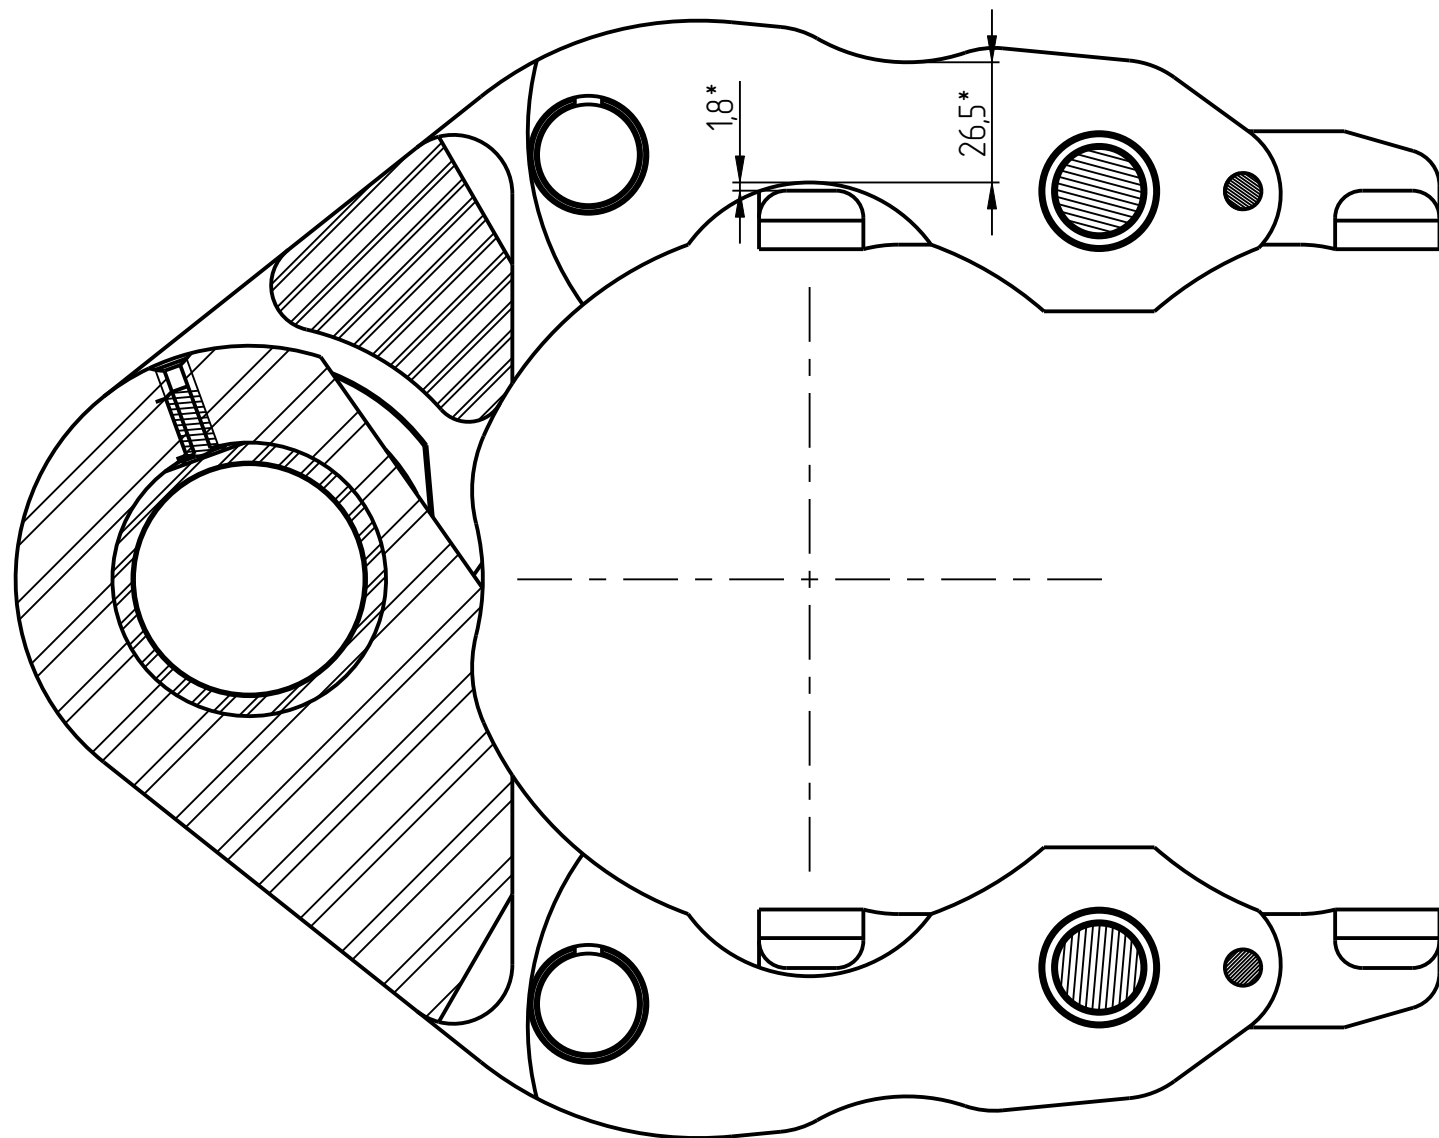


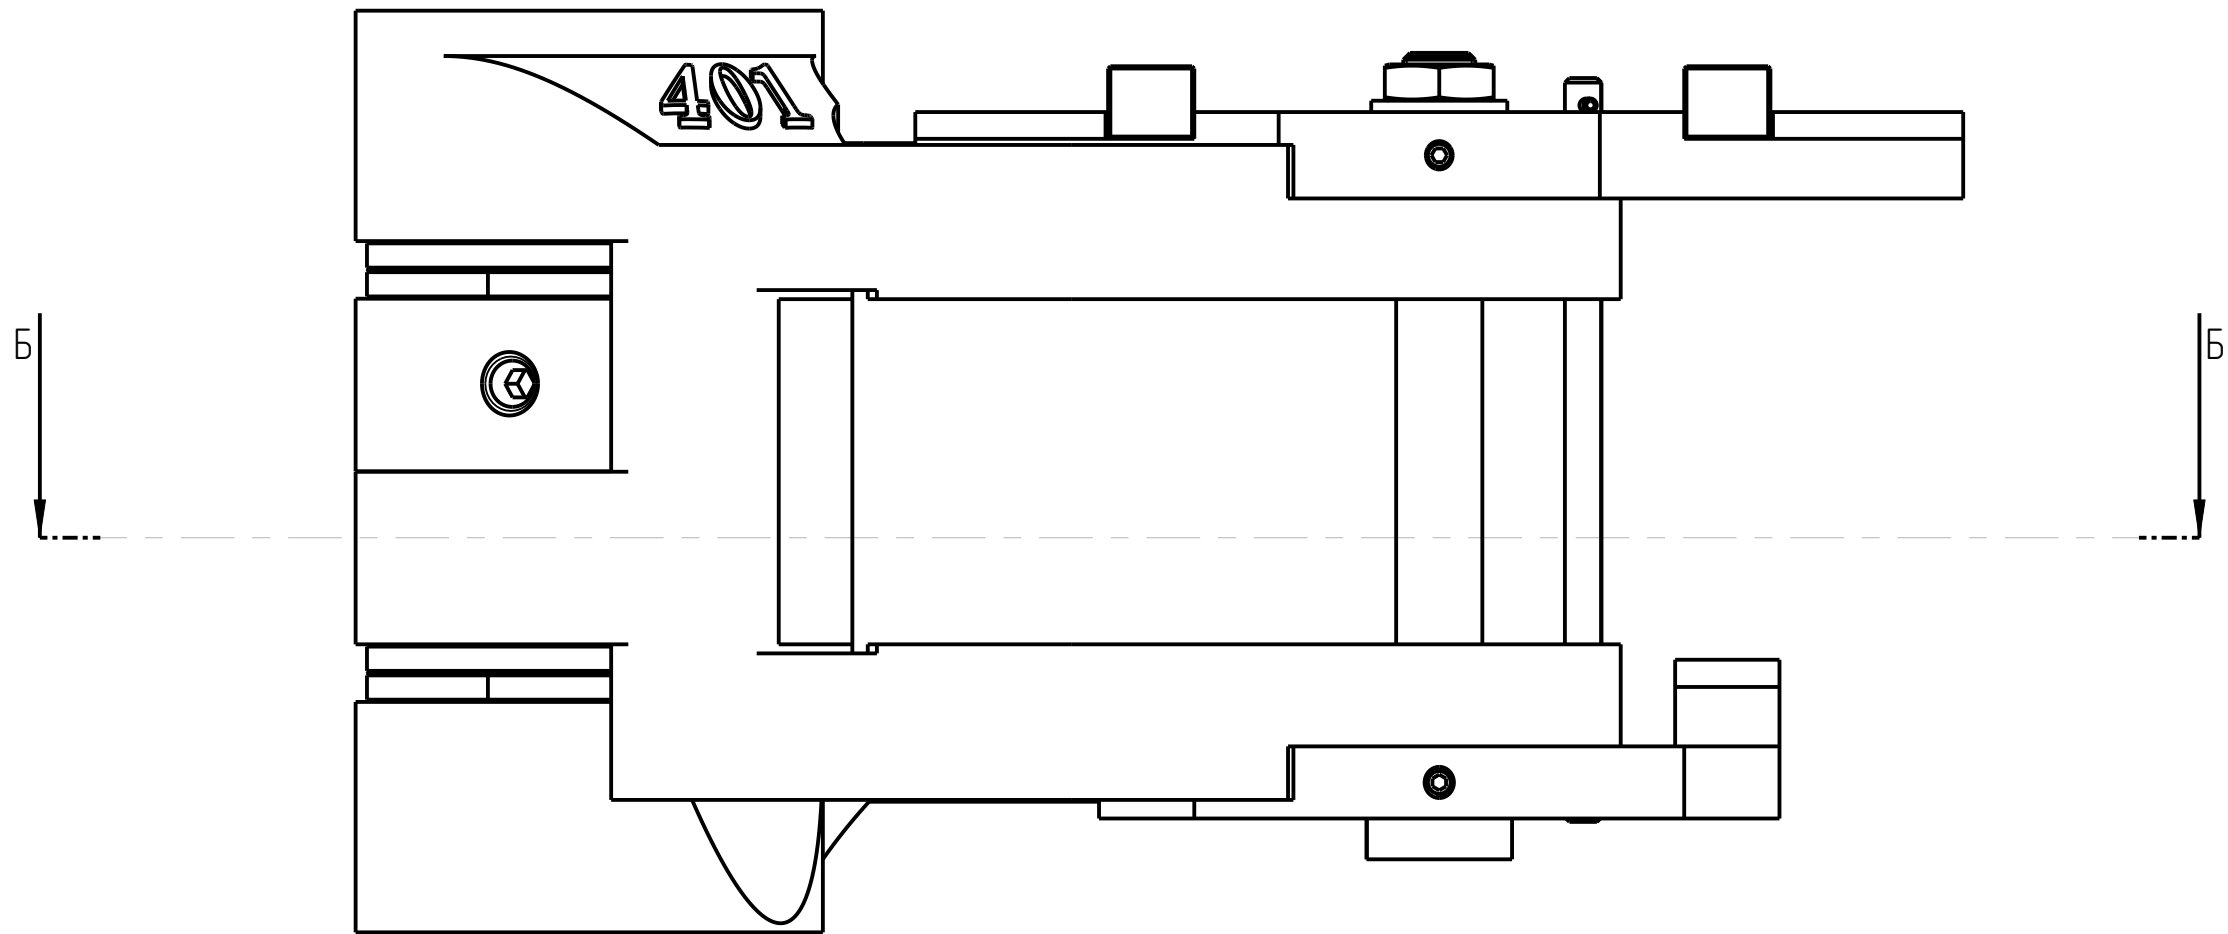

Б-Б

Изм.	Лист	И докум.	Подп.	Дата