



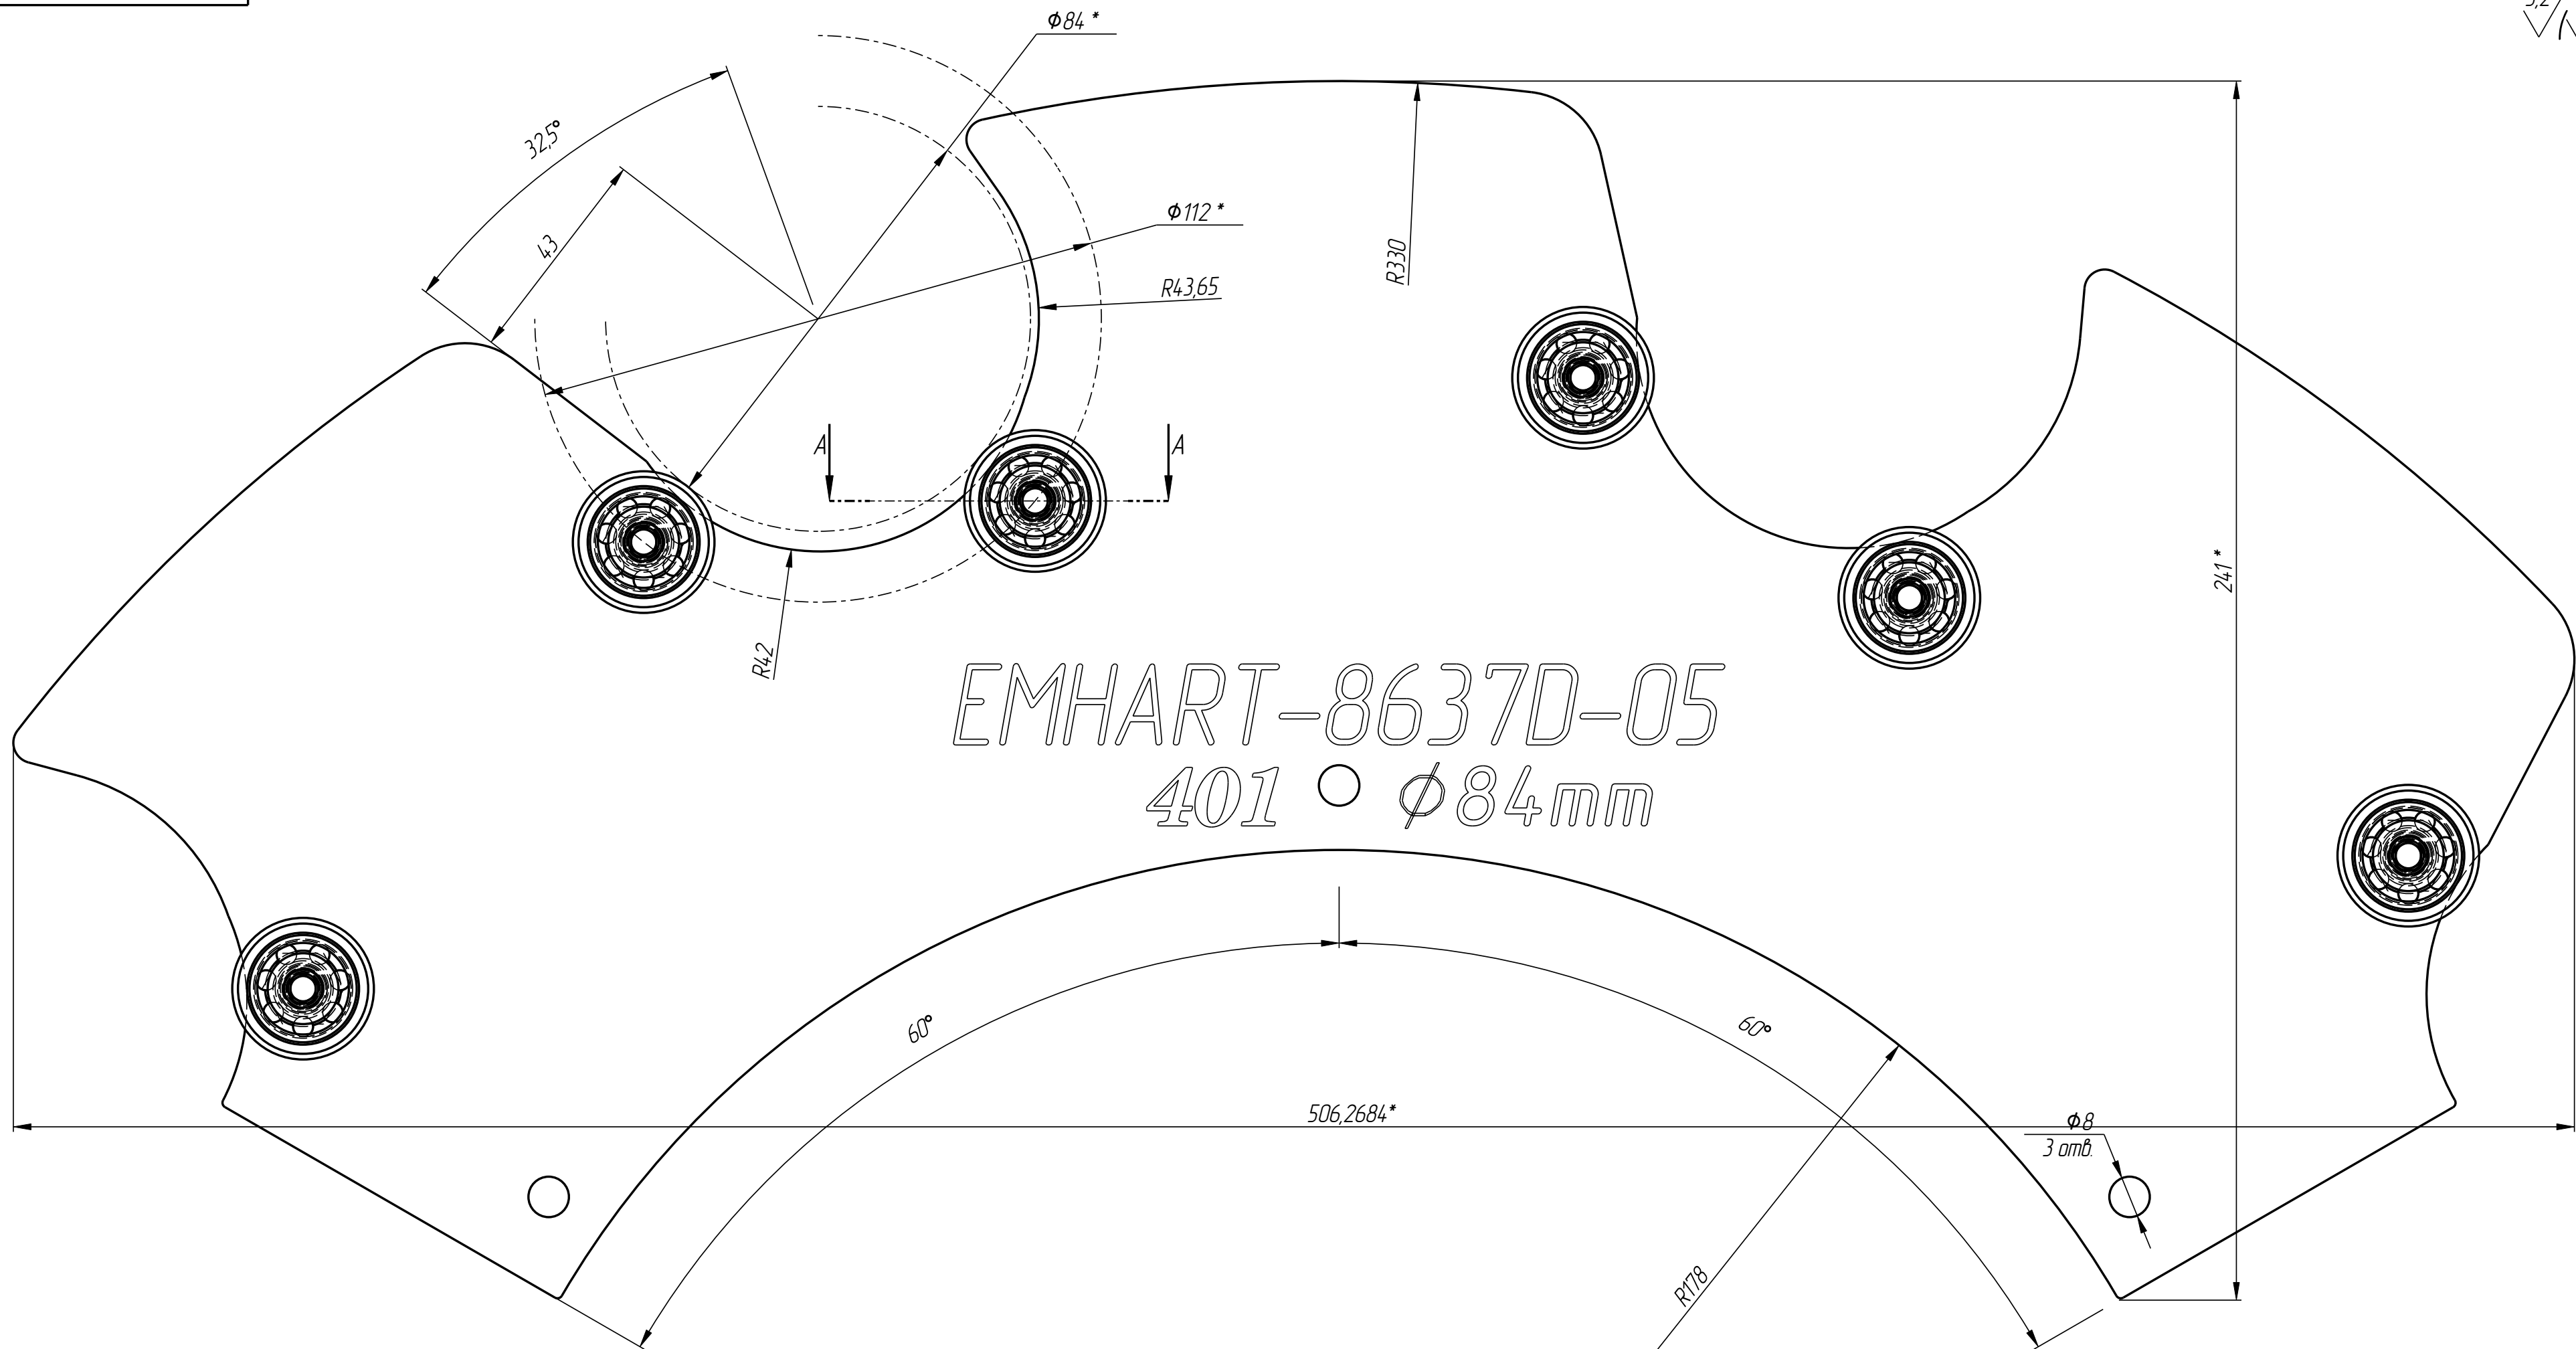

EMHART-8637D-05  
401 Ø84mm

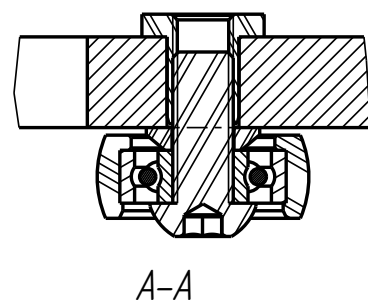

|    |   |                 |                                                           |                   |  |  |
|----|---|-----------------|-----------------------------------------------------------|-------------------|--|--|
|    |   |                 |                                                           | Документация      |  |  |
| A3 |   |                 | EMHART-8637D_SB-05-D84 Сборка                             | Сборочный чертеж  |  |  |
|    |   |                 |                                                           | Сборочные единицы |  |  |
| A3 | 1 | 10-STD-R2       | Ролик в сборе для Emhart                                  | 6                 |  |  |
|    |   |                 |                                                           |                   |  |  |
|    |   |                 |                                                           | Детали            |  |  |
| A3 | 2 | EMHART-8637D-05 | Сектор звезды Emhart Ø 76-130мм с роликом Ø 28 9 карманов | 1                 |  |  |
|    |   |                 |                                                           |                   |  |  |
|    |   |                 |                                                           |                   |  |  |
|    |   |                 |                                                           |                   |  |  |

|          |      |          |       |          |  |                               |           |       |         |
|----------|------|----------|-------|----------|--|-------------------------------|-----------|-------|---------|
|          |      |          |       |          |  | EMHART-8637D_SB-05-D84 Сборка |           |       |         |
| Изм.     | Лист | № докум. | Подп. | Дата     |  | Звезда Emhart                 | Лист      | Масса | Масштаб |
| Разраб.  |      |          |       | 09.06.25 |  |                               |           | 1,2   | 1:1     |
| Проб.    |      |          |       |          |  |                               | Лист      | 1     | Листов  |
| Т.контр. |      |          |       |          |  |                               |           |       | 1       |
| Нач.отд. |      |          |       |          |  |                               | ООО "ПТО" |       |         |
| Н.контр. |      |          |       |          |  |                               |           |       |         |
| Утв.     |      |          |       |          |  |                               |           |       |         |