


Инв. № подл.		Подп. и дата	Взам. инв. №	Инв. № дудл.	Подп. и дата	Справ. №		Перв. примен.

УСГ-4520-001-05 Деталь

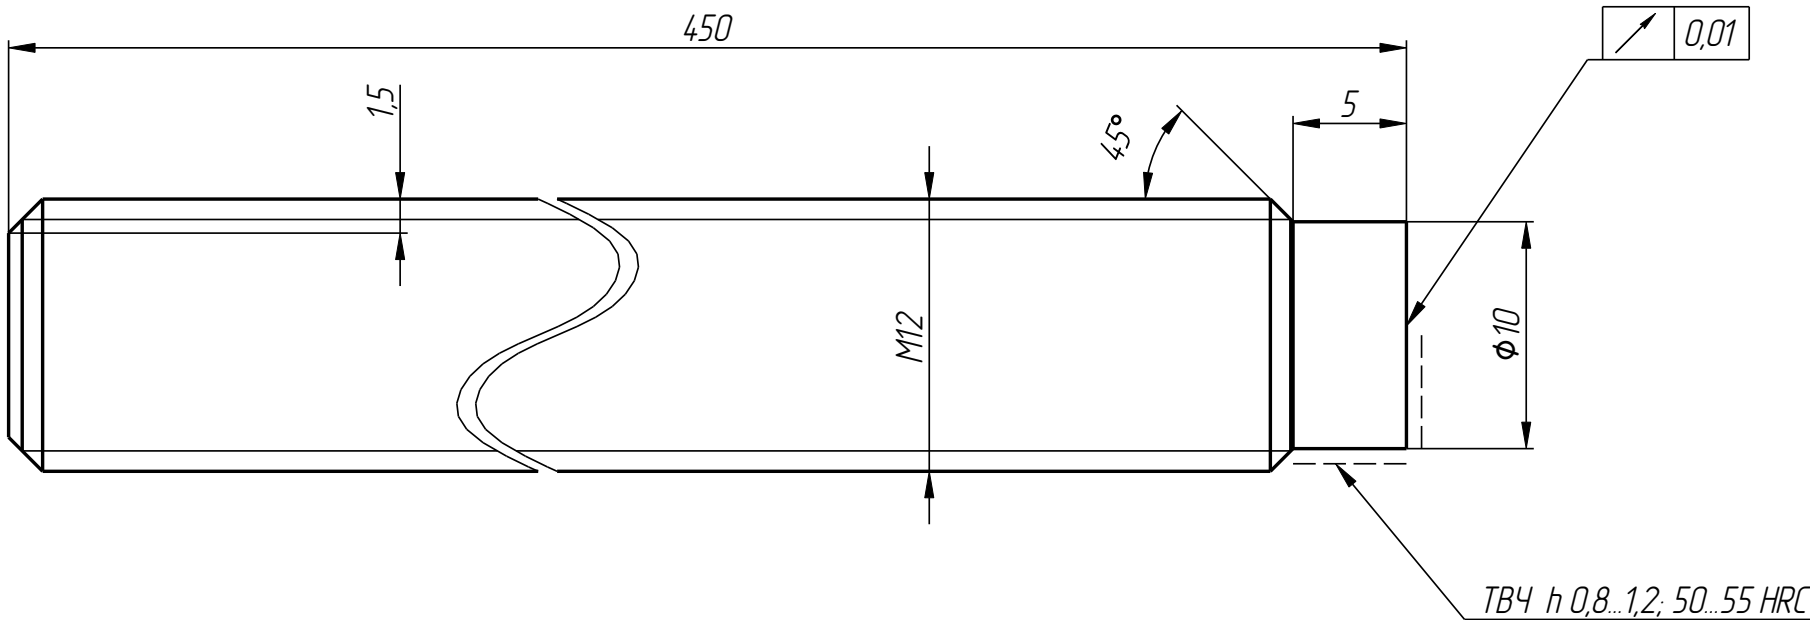

Заготовка- Строительная шпилька М12!

					УСГ-4520-001-05 Деталь				
Изм.	Лист	№ докум.	Подп.	Дата	Палец	Лит.		Масса	Масштаб
Разраб.			11.09.23					0,30	3:1
Пров									
Т.контр.						Лист	1	Листов	1
Нач.отд.									
Н.контр.					Сталь 40Х ГОСТ4593-71	ООО "ПТО"			
Утв.									