
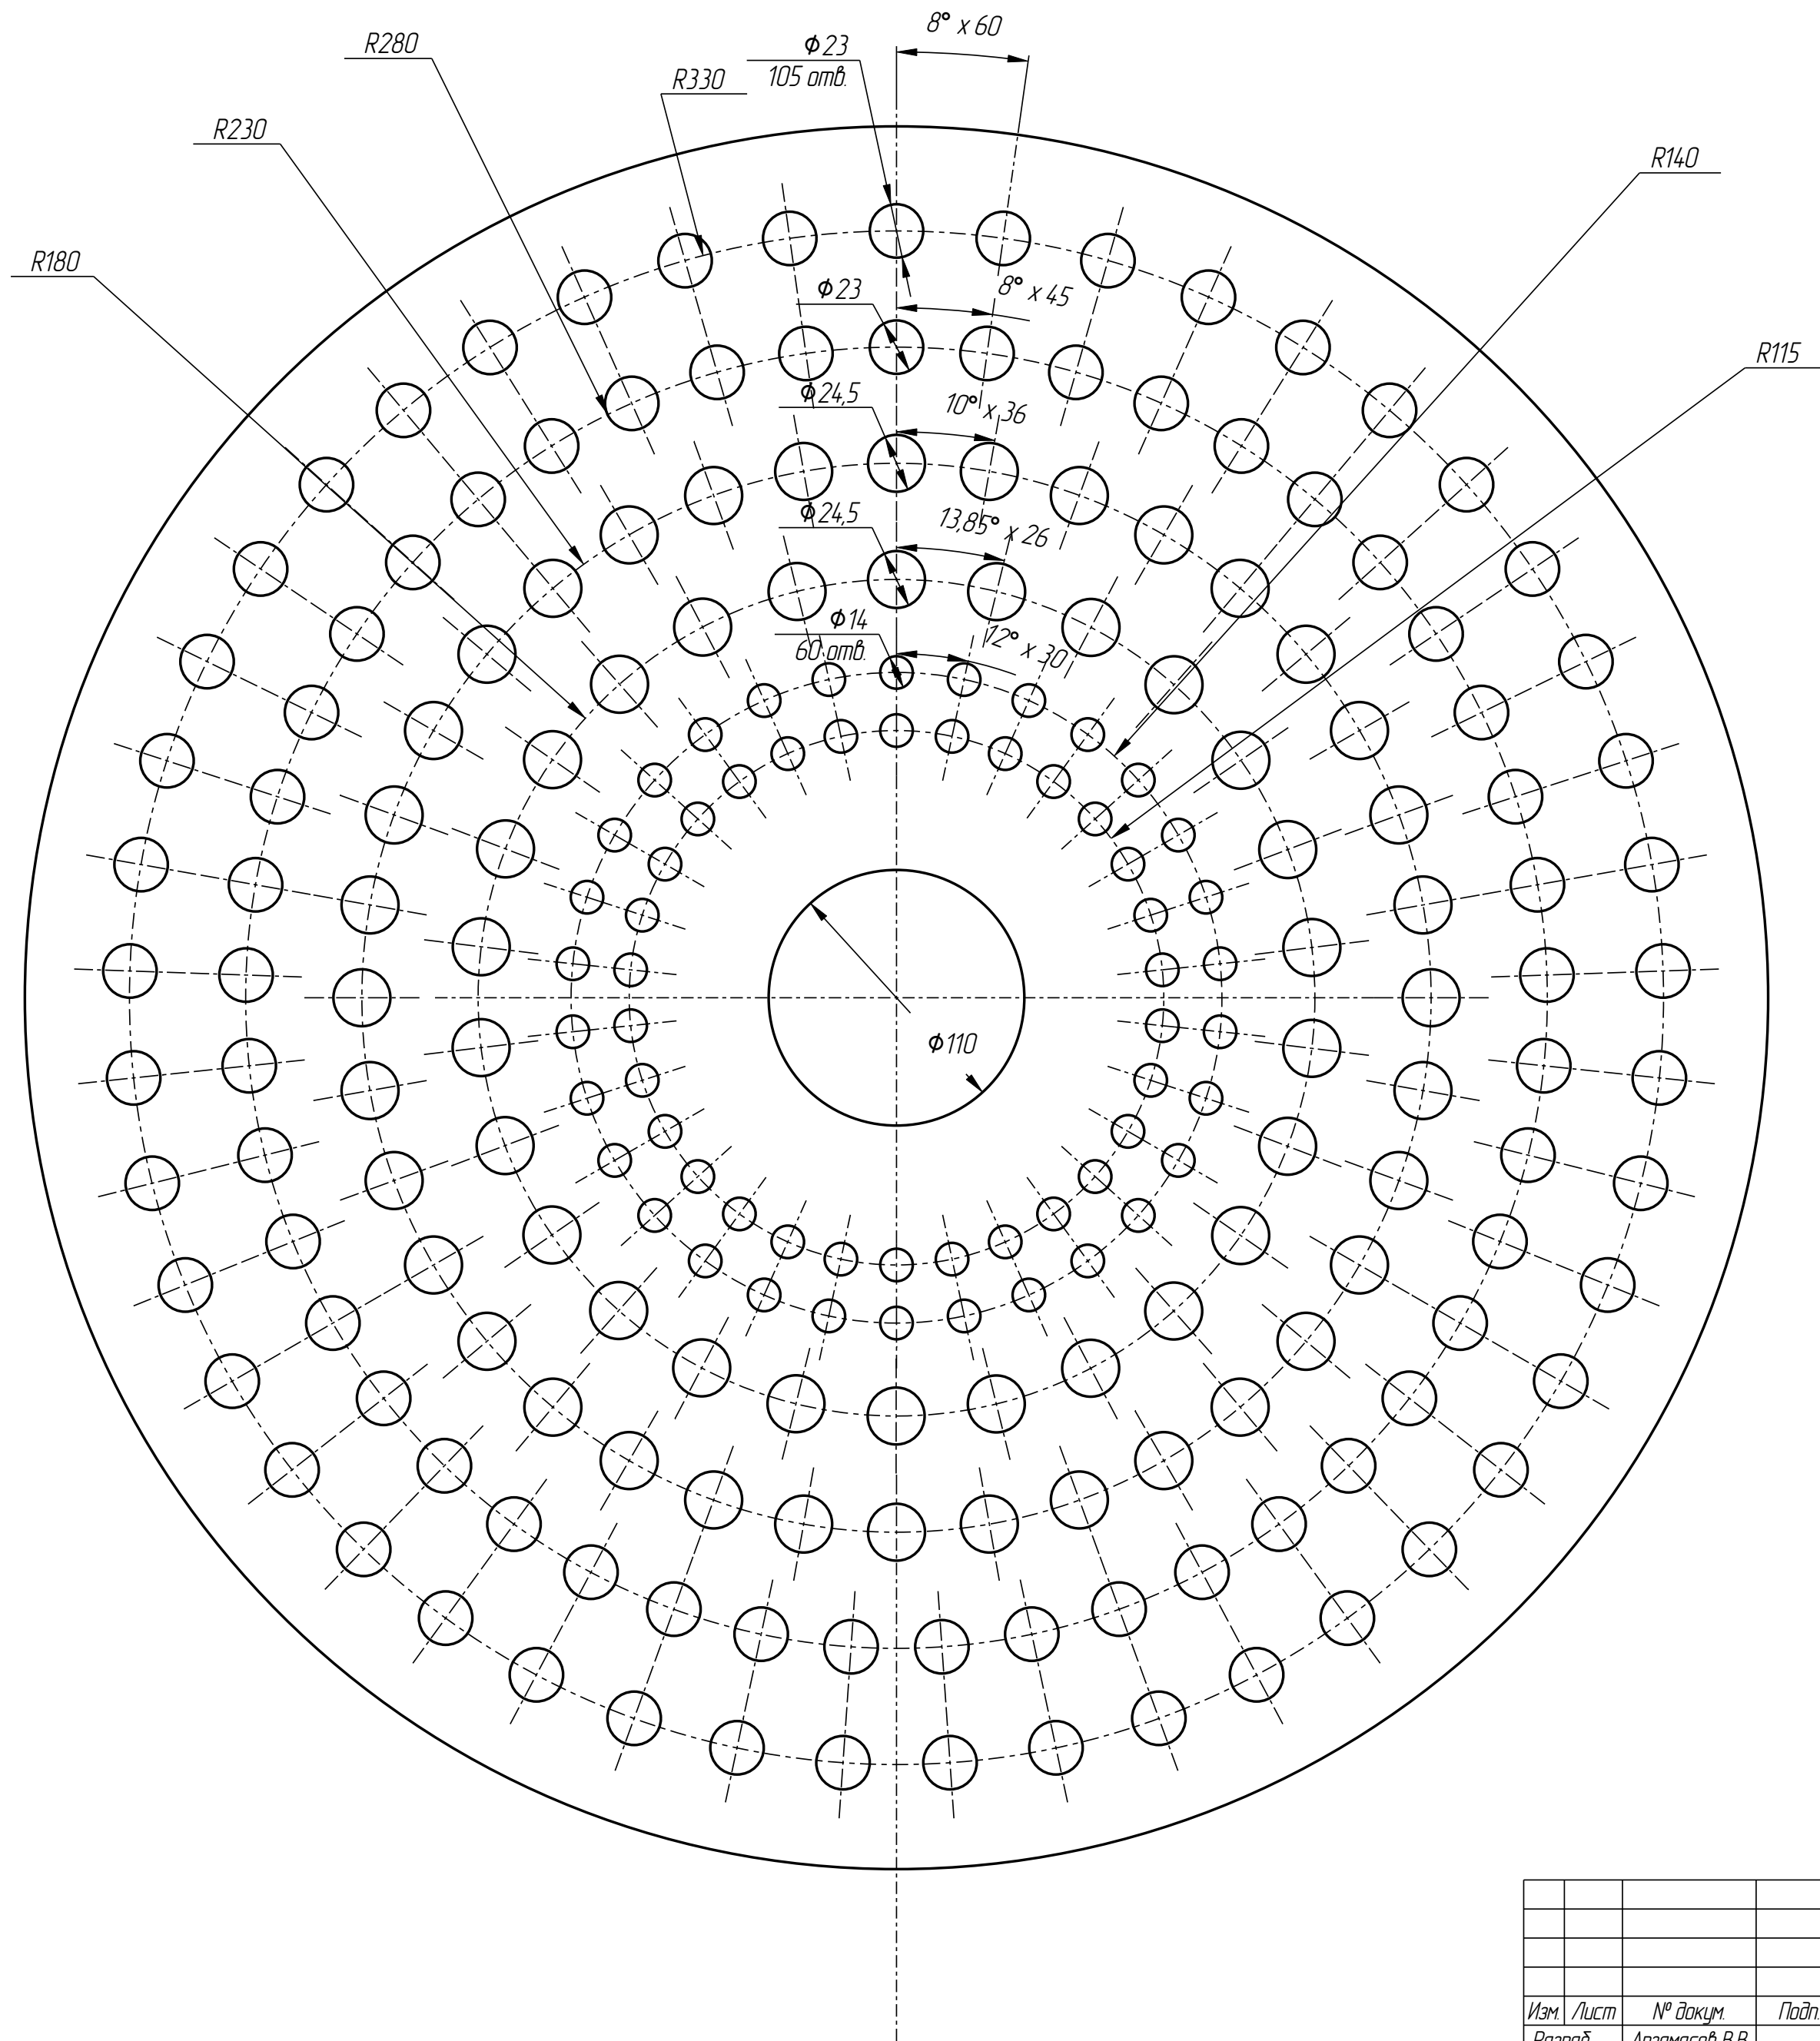


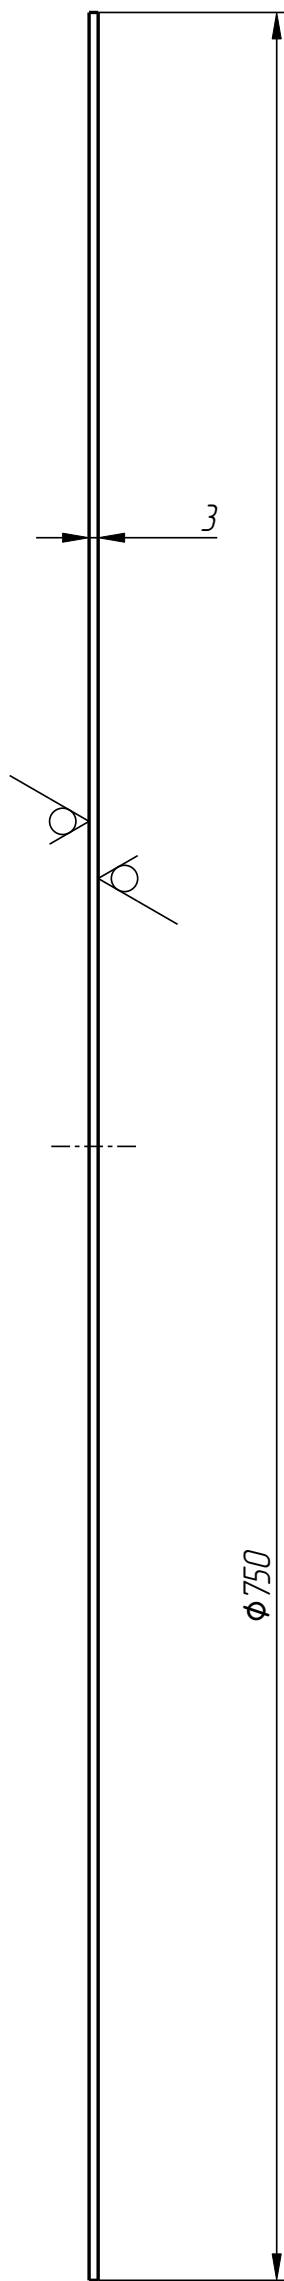

Перв. примен.
Спроб. N

Подп. и дата
Инф. N подл.
Взам. инф. N
Подп. и дата
Инф. N подл.

КТП-800-1250-20-02 Деталь					
Изм.	Лист	№ докум.	Подп.	Дата	Дно
Разраб.	Арзамасов В.В.	25.07.25			
Проб.					
Т.контр.					
Нач.отд.					Лист 1 / Листов 1
Н.контр.					
Утв.					Сталь 20Х23Н18 ГОСТ 5632-72
Копировал:					000 "ПТО"
Формат: А2					