


Перв. примен.	Спроб. N	Подп. и дата	Инф. N доп.	Взам. инф. N	Подп. и дата	Инф. N подл.

КТП-900-1500-00-12-Z Деталь

6,3/
√N

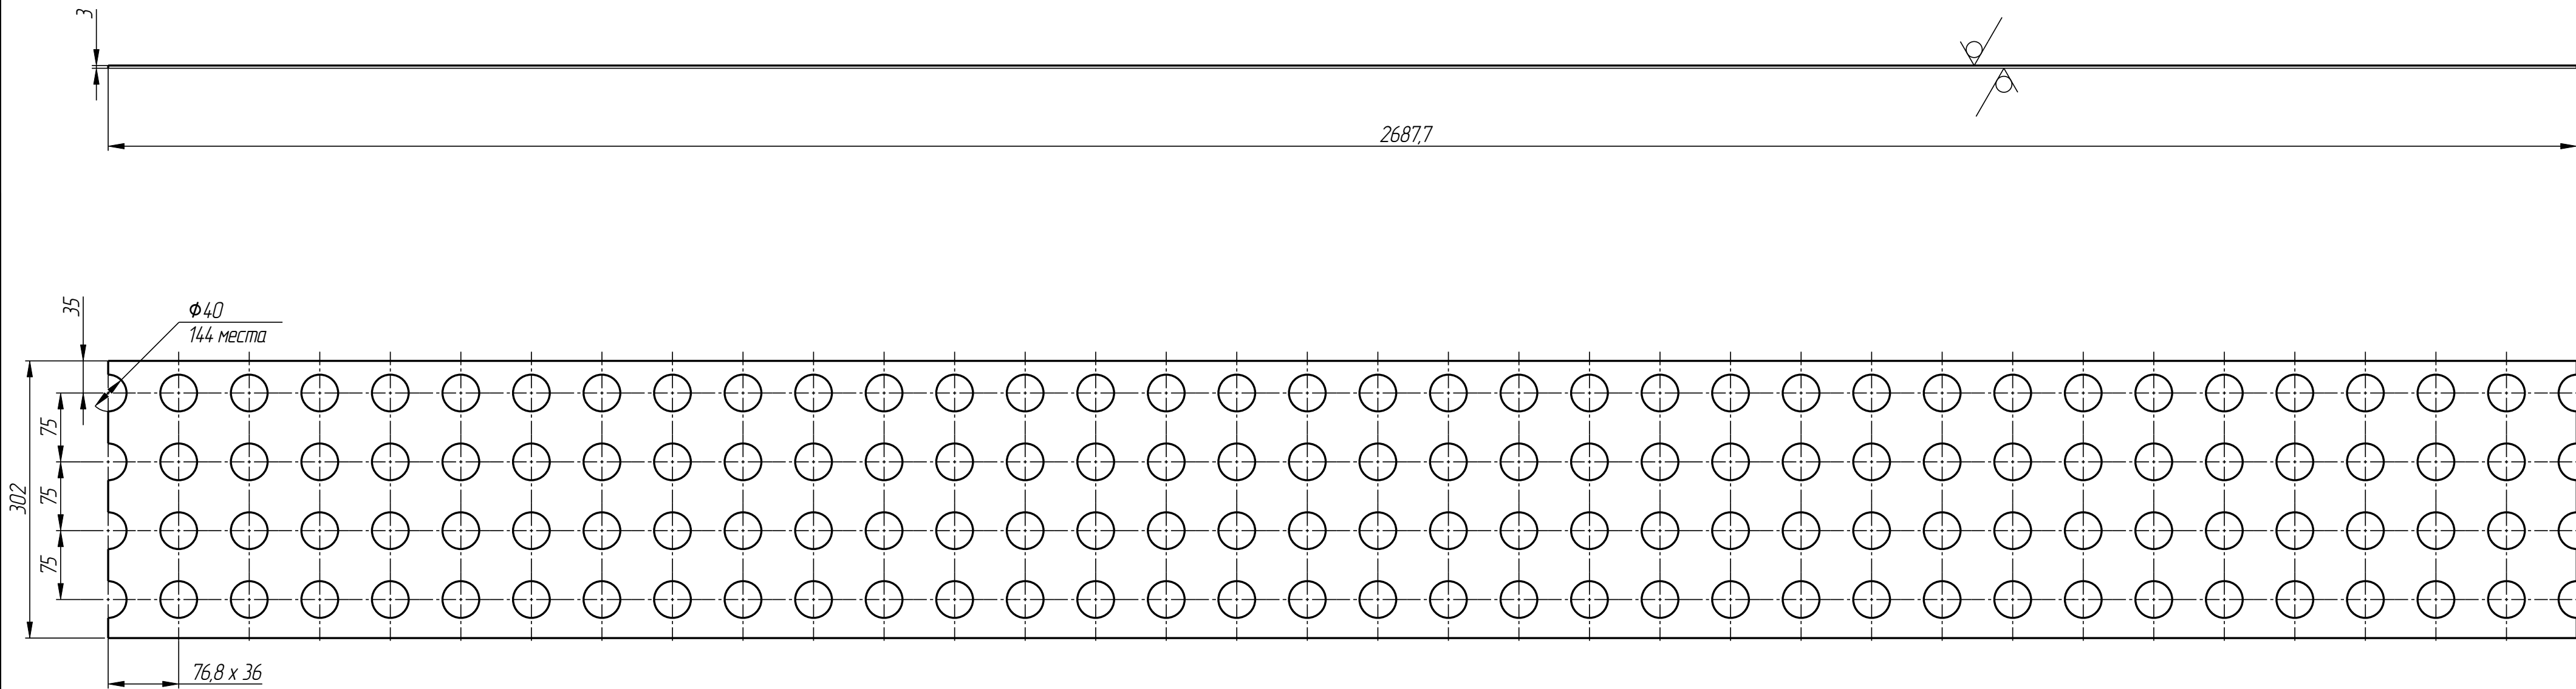

Примечание: Допускается изготовление сварной из нескольких частей.

- 1. * – размеры для справок;
- 2. Н14, h14, ±IT14/2;
- 3. Неуказанные фаски– 0,5х45°, радиусы– R0,3;
- 4. Острые кромки притупить.

					КТП-900-1500-00-12-Z Деталь				
					Обработка заготовка (развертка)	Лит.		Масса	Масштаб
Изм.	Лист	№ докум.	Подп.	Дата				15,1	1:5
Разраб.	Арзамасов В.В.			02.05.23					
Проб.									
Т.контр.						Лист	1	Листов	1
Нач.отд.						000 "ПТО"			
Н.контр.									
Утв.					Сталь 20Х23Н18 ГОСТ 5632-72				