


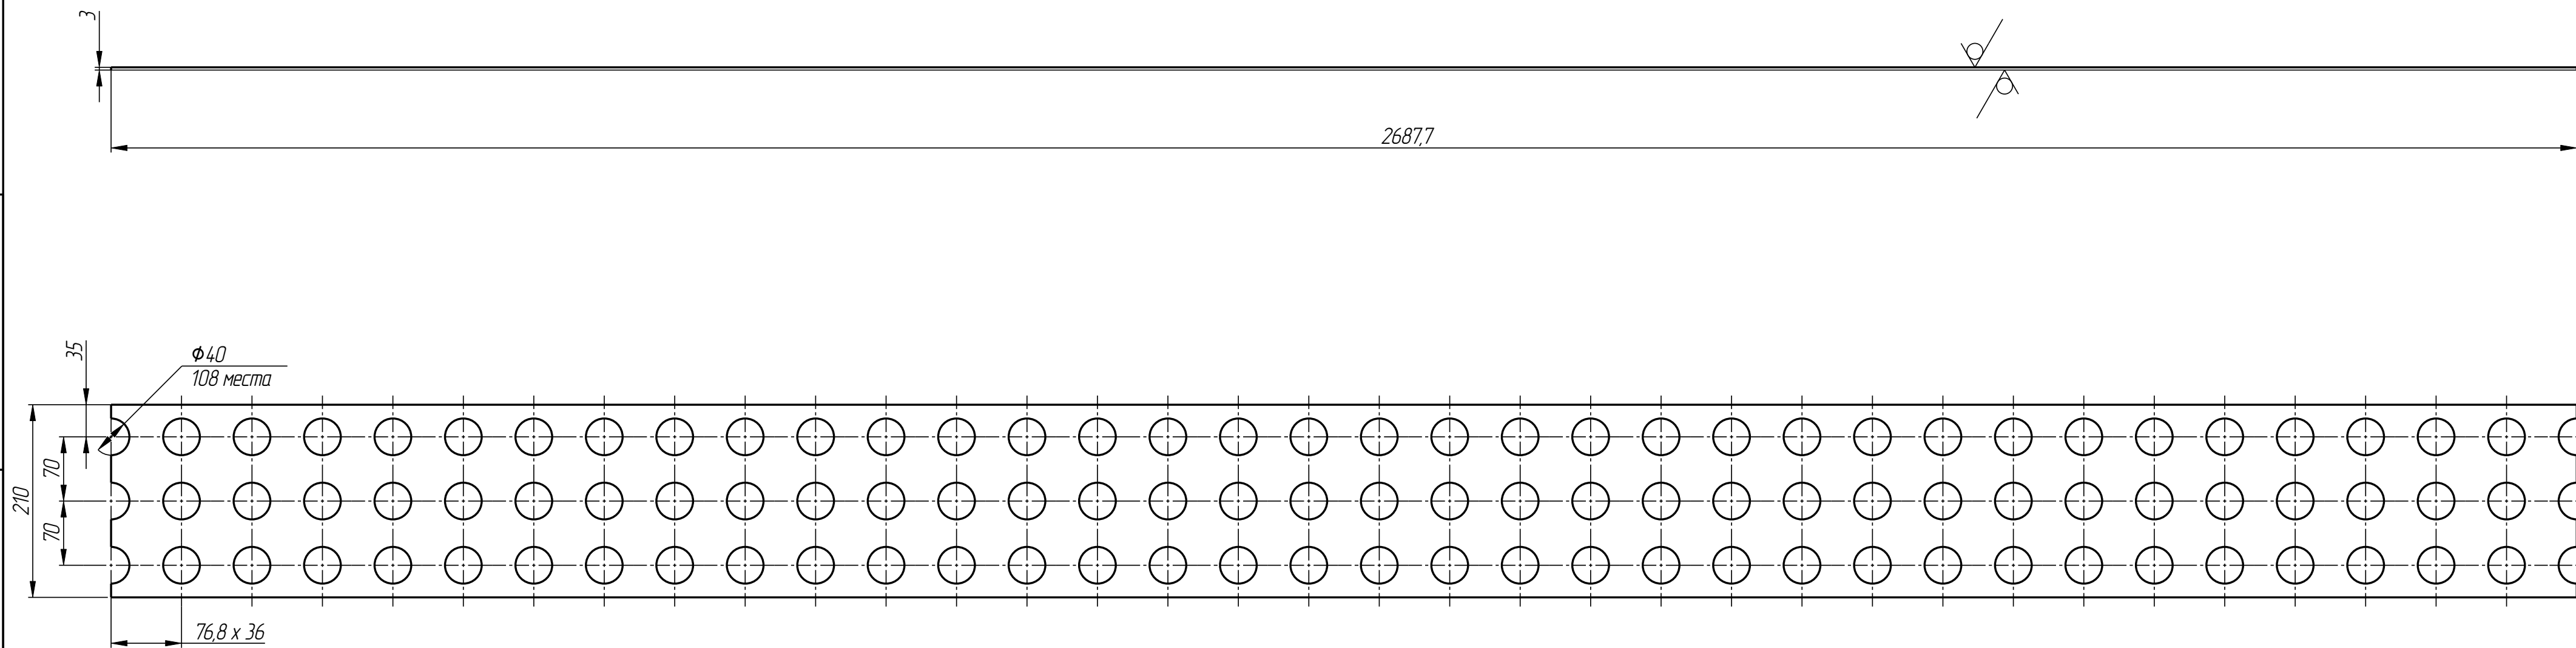

Примечание: Допускается изготовление сварной из нескольких частей.

1. * – размеры для справок;
2. H14, h14, $\pm IT14/2$;
3. Неуказанные фаски – $0,5 \times 45^\circ$, радиусы – $R0,3$;
4. Острые кромки притупить.

					КТП-900-1500-20-04-Z Деталь				
Изм	Лист	№ докум	Подп	Дата	Обучайка 2 заготовка (развертка)	Лист		Масса	Масштаб
Разраб	Арзамасов В.В.			02.05.23				10,3	1:5
Проб									
Т.контр						Лист	1	Листов	1
Нач.отд									
Н.контр					Сталь 20Х23Н18 ГОСТ 5632-72	ООО "ПТО"			
Утв									