


Перв. примен.		Справ. №		Подп. и дата		Взам. инв. №		Инв. № дубл.		Подп. и дата		Инв. № подл.	

КТП-900-1500-20-05 Деталь

6,3
✓/M

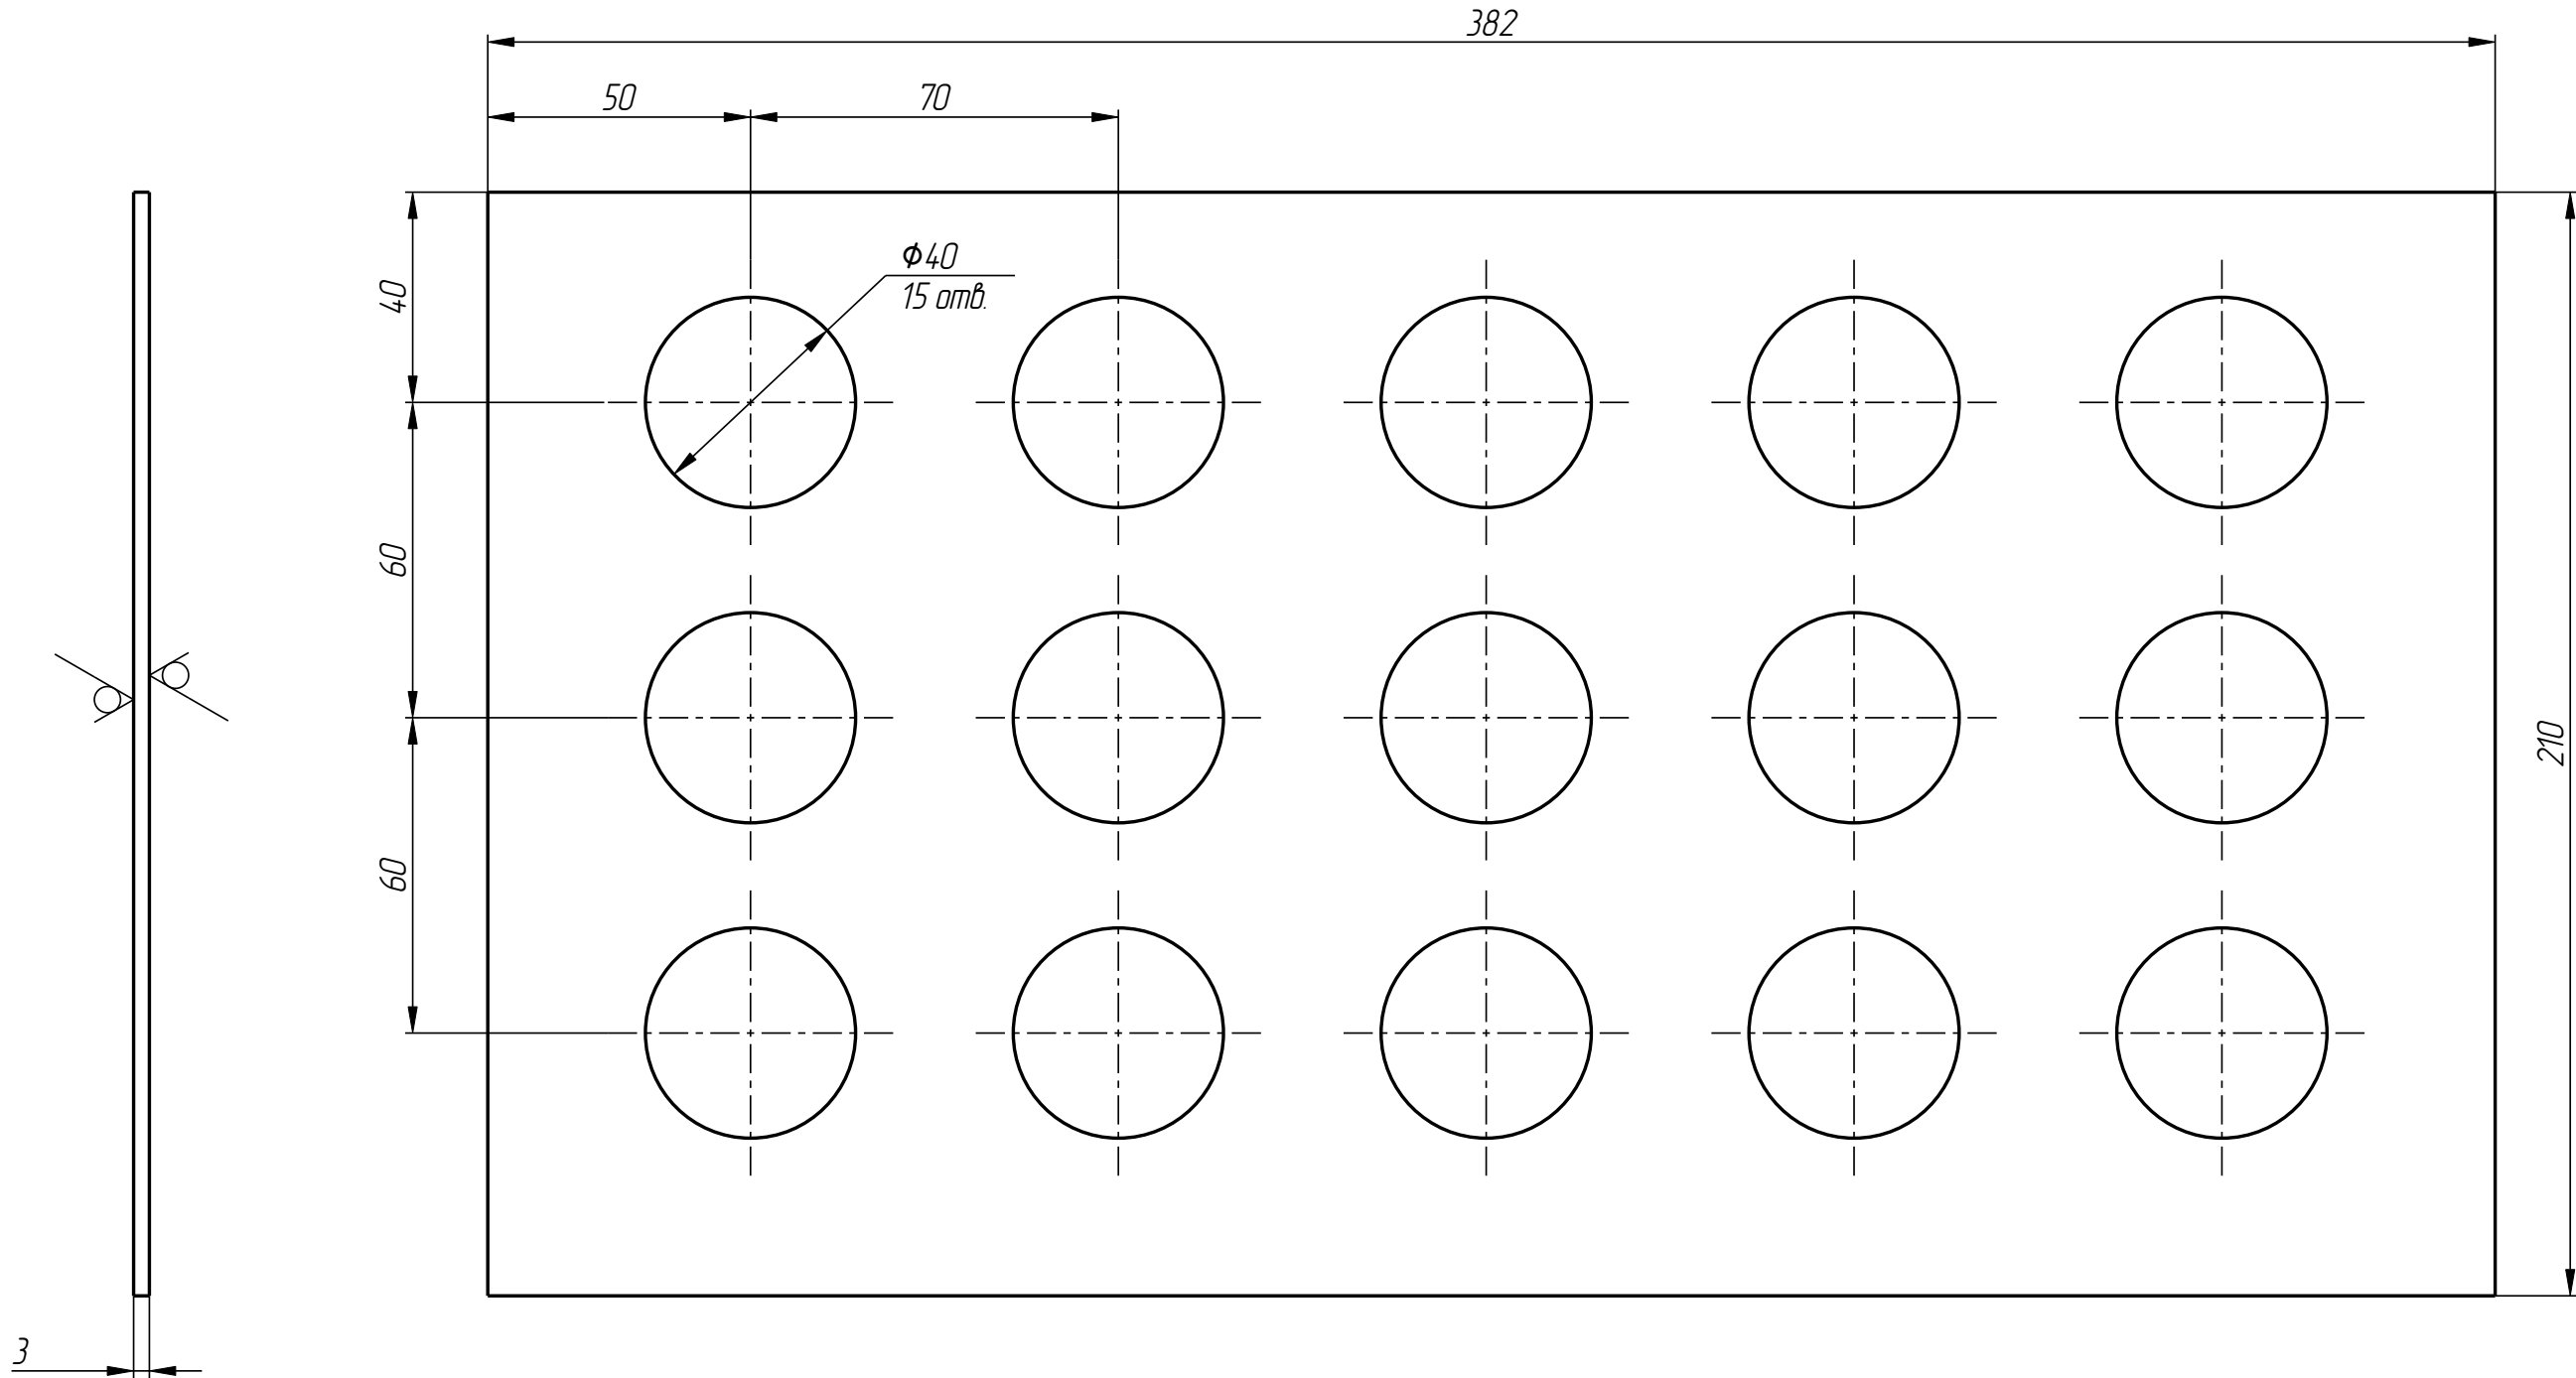

1. * - размеры для справок;
2. Предельные отклонения по Н14; h14; ±IT14/2;
3. Неуказанные фаски- 0.5х45°, радиусы- R0.5 мм.

					КТП-900-1500-20-05 Деталь				
Изм.	Лист	№ докум.	Подп.	Дата	Перегородка 2	Лит.		Масса	Масштаб
Разраб.	Арзамасов В.В.		02.05.23					1,5	7:10
Пров									
Т.контр.						Лист	1	Листов	1
Нач.отд.									
Н.контр.					Сталь 20Х23Н18 ГОСТ 5632-72		ООО "ПТО"		
Утв.									