


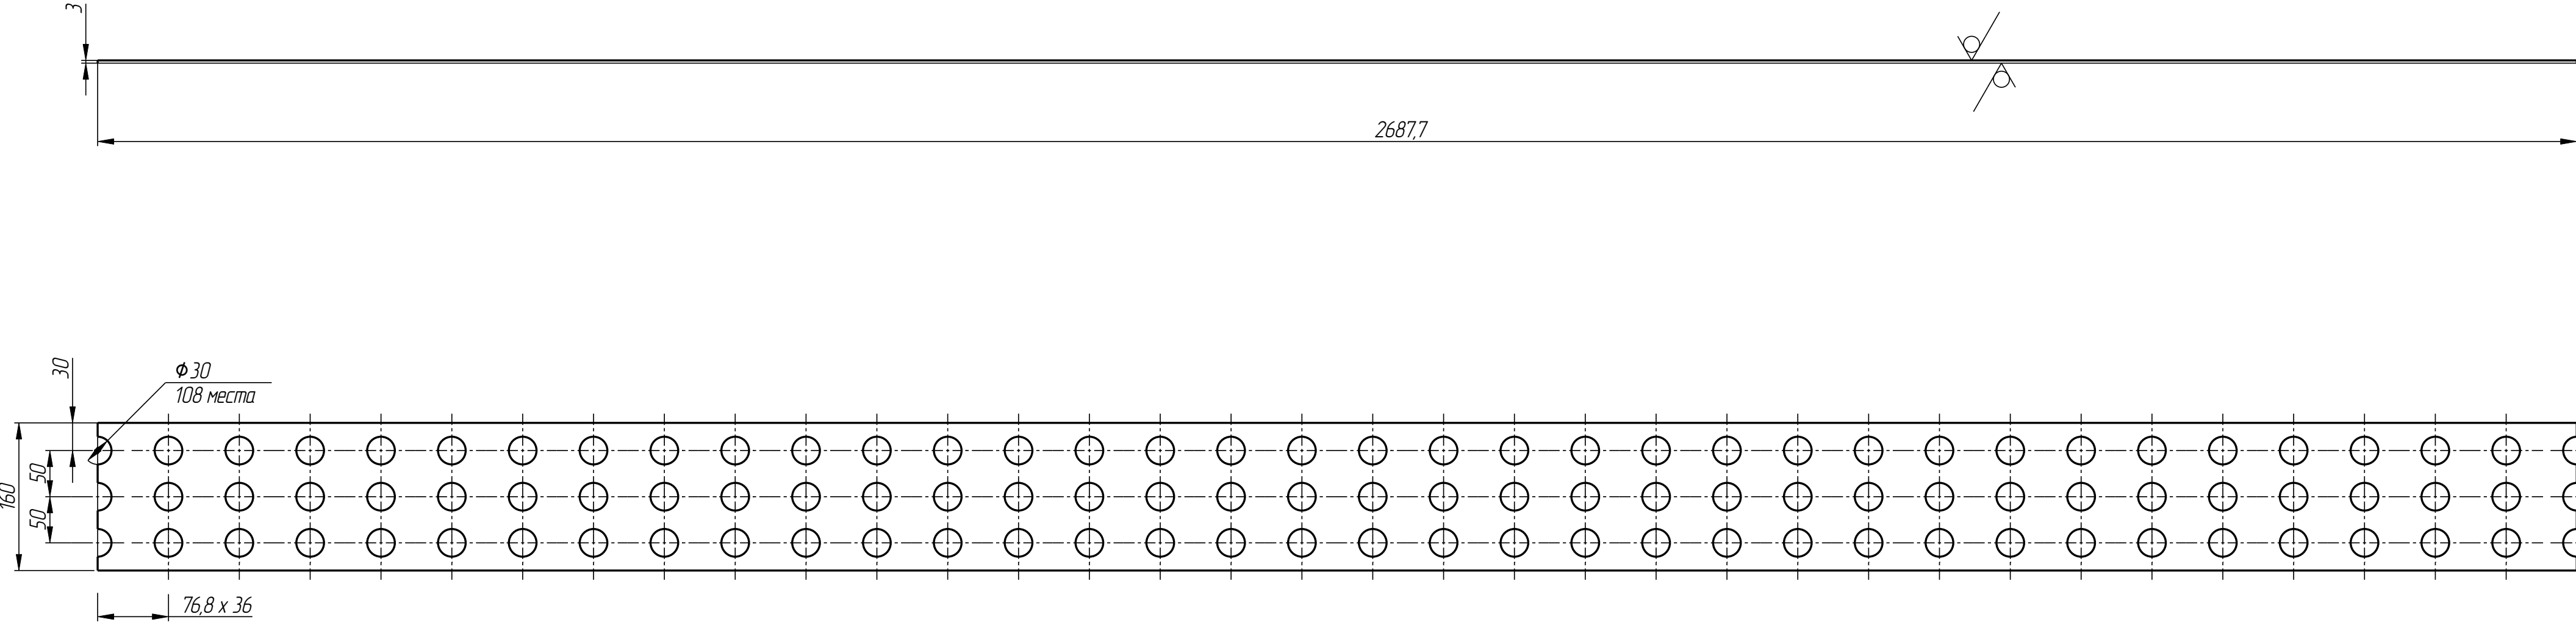

Примечание: Допускается изготовление сварной из нескольких частей.

1. * – размеры для справок;
2. H14, h14, $\pm IT14/2$;
3. Неуказанные фаски– 0,5х45°, радиусы– R0,3;
4. Острые кромки притупить.

Перв. примен.	
Спроб. N	
Подп. и дата	
Инф. N доп.	
Взам. инф. N	
Подп. и дата	
Инф. N подл.	

					КТП-900-1500-30-04-Z Деталь						
					Общая 3 заготовка (развертка)	Лит.		Масса	Масштаб		
Изм.	Лист	№ докум.	Подп.	Дата				8,4	1:5		
						Лист		1	Листов	1	
Разраб.					Арзамасов В.В.					02.05.23	
Пров.											
Т.контр.											
Нач.отд.											
Н.контр.											
Утв.											
					Сталь 20Х23Н18 ГОСТ 5632-72					ООО "ПТО"	