


Перв. примен.		Справ. №		Подп. и дата		Взам. инв. №		Инв. № дудл.		Подп. и дата		Инв. № подл.	

КТП-900-1500-30-05 Деталь

6,3/
√M

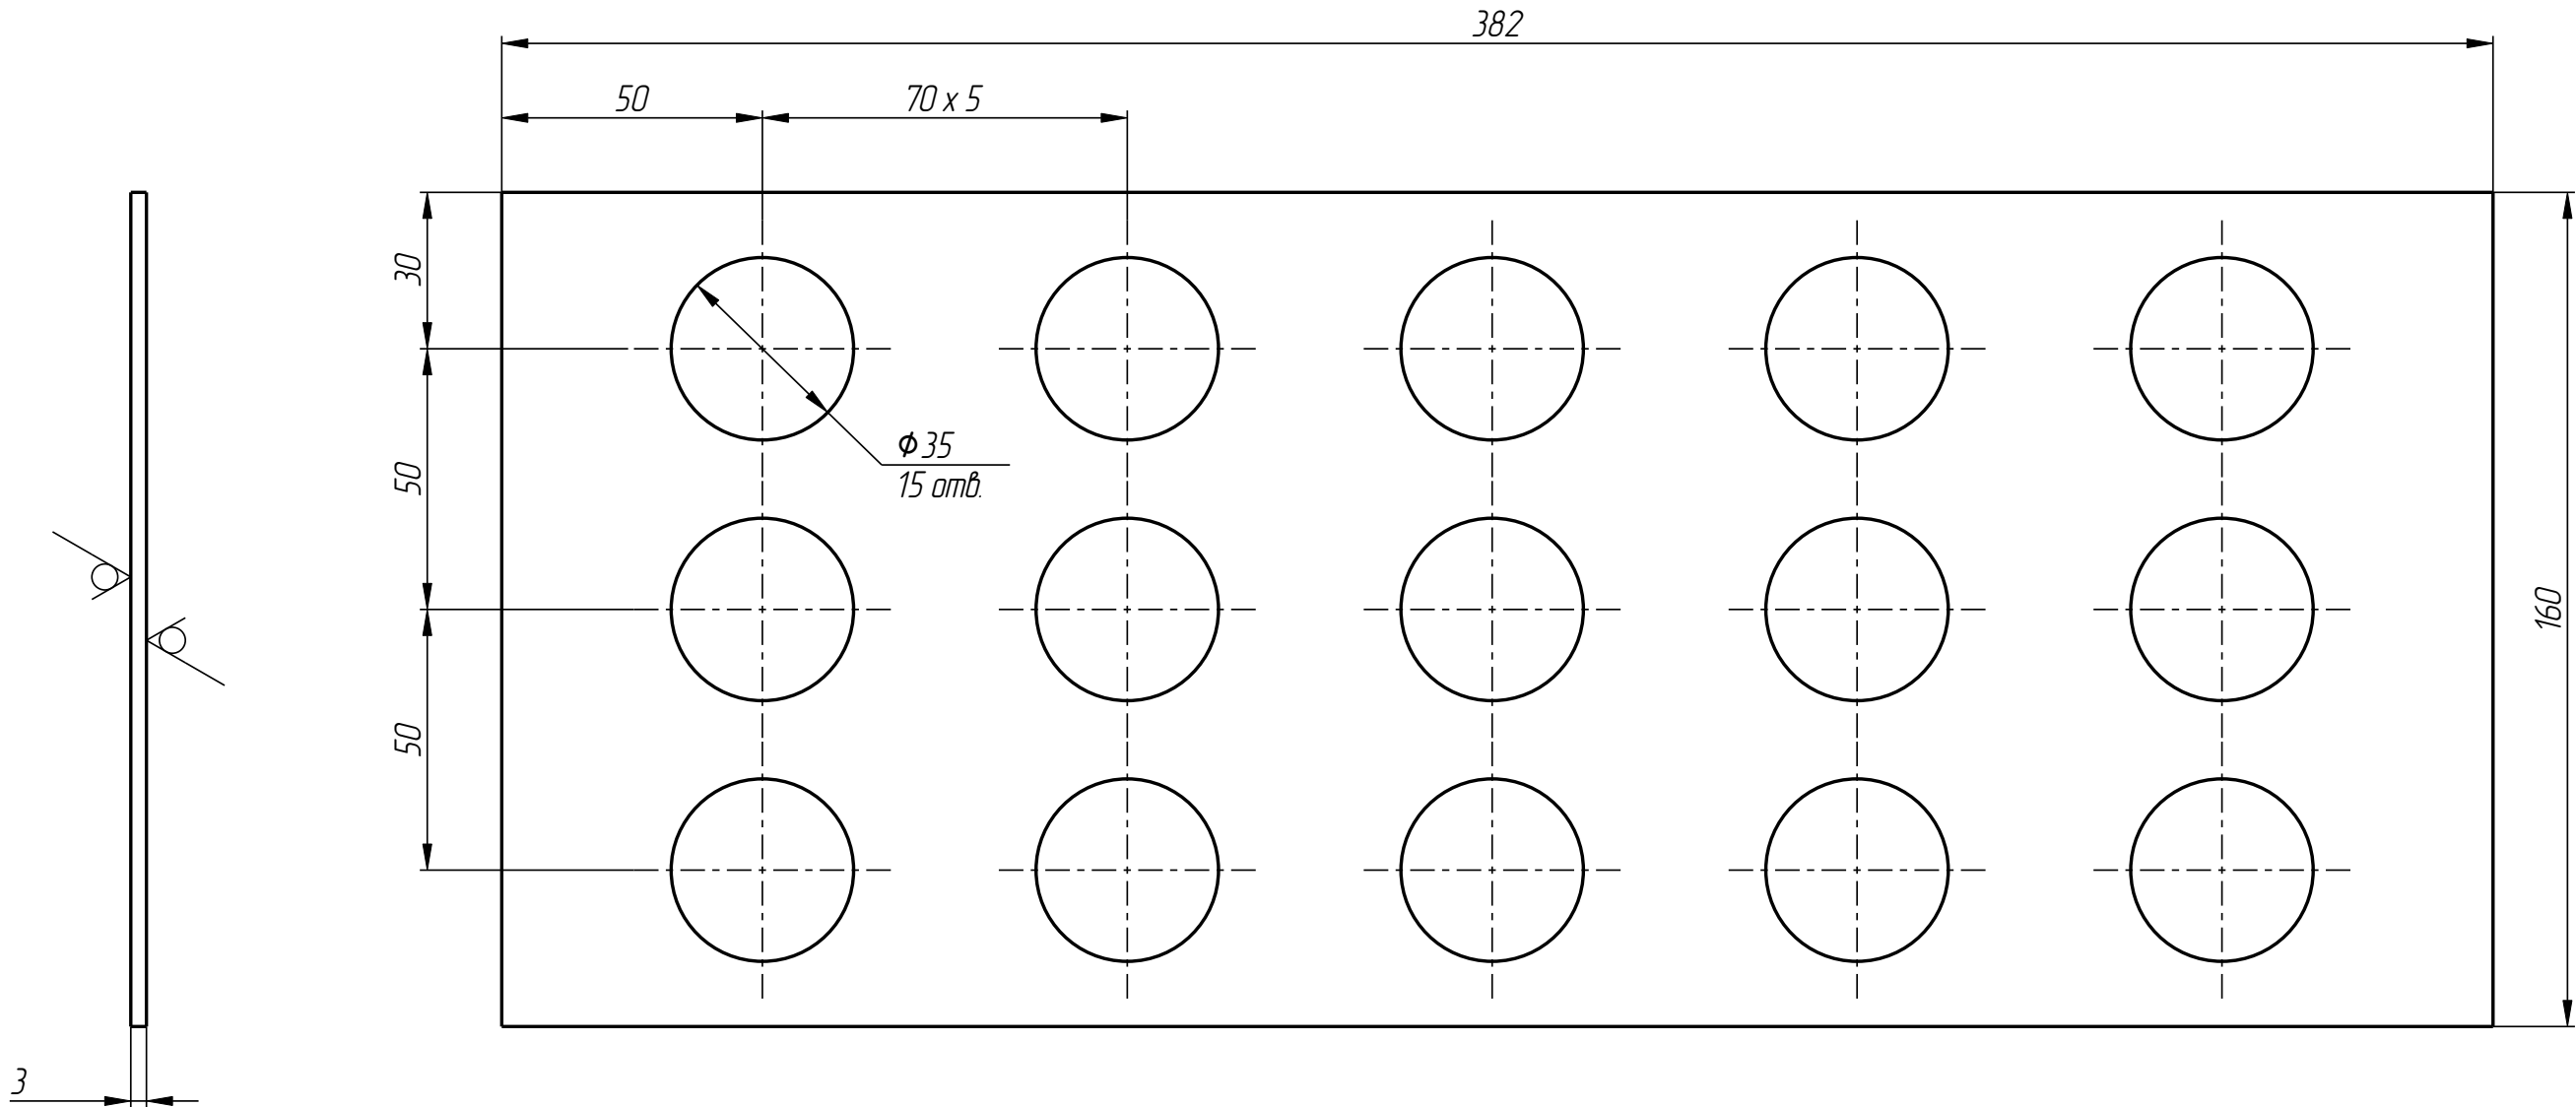

1. * – размеры для справок;
2. Предельные отклонения по Н14; h14; ±IT14/2;
3. Неуказанные фаски – 0.5x45°, радиусы – R0.5 мм.

					КТП-900-1500-30-05 Деталь									
Изм.	Лист	№ докум.	Подп.	Дата	Перегородка 3			Лит.	Масса	Масштаб				
Разраб.	Арзамасов В.В.		02.05.23							1,1	7:10			
Пров														
Т.контр.								Лист	1	Листов	1			
Нач.отд.								Сталь 20Х23Н18 ГОСТ 5632-72						
Н.контр.					ООО "ПТО"									
Утв.														